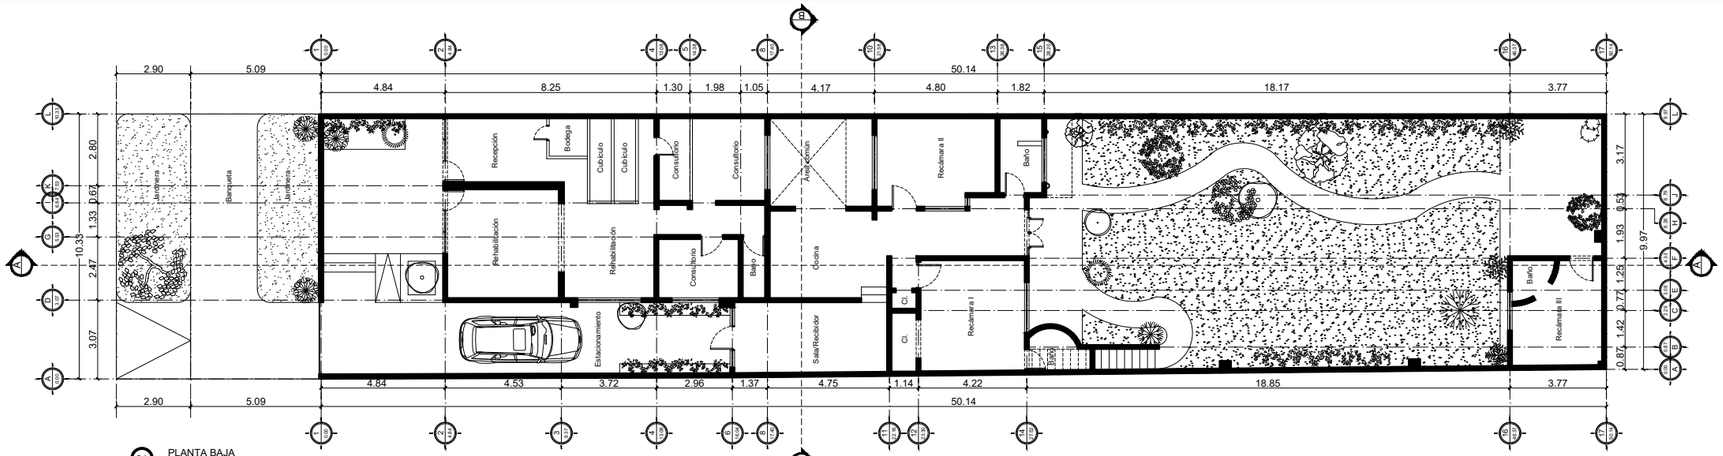

01 PLANTA BAJA
ESCALA 1:100

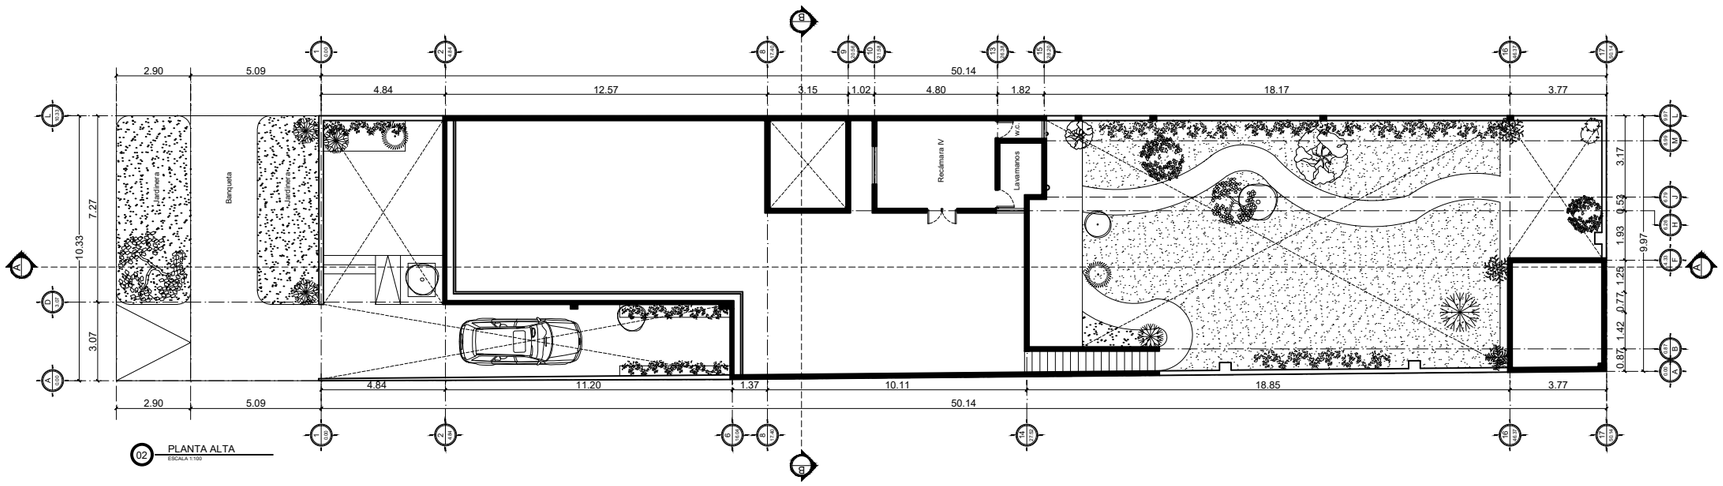

02 PLANTA ALTA
ESCALA 1:100

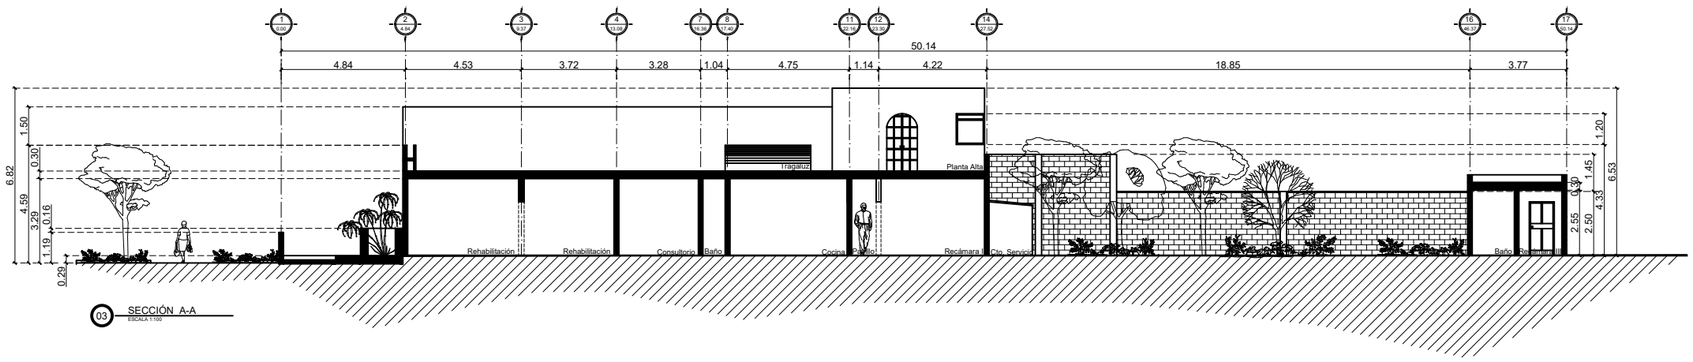

03 SECCIÓN A-A
ESCALA 1:100

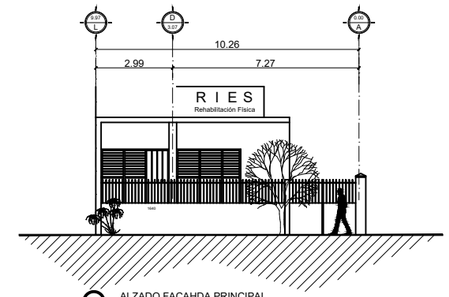

04 ALZADO FACAHDA PRINCIPAL
ESCALA 1:100

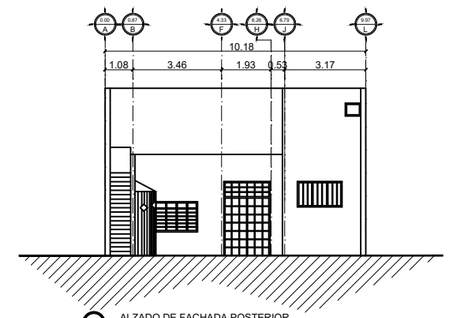

05 ALZADO DE FACHADA POSTERIOR
ESCALA 1:100

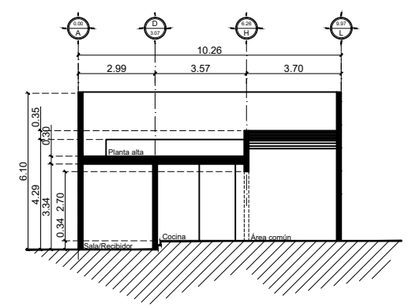

06 SECCIÓN B-B
ESCALA 1:100

ATELIER LR DISEÑO Y CONSTRUCCIÓN BUENOS AIRES #2775 COL. PROVIDENCIA GUADALAJARA, JALISCO. C.P. 44639	TITULO DEL PLANO. LEVANTAMIENTO	ÚBICACIÓN: AV. ESPAÑA 1640, MODERNA, 44190 GUADALAJARA, JALISCO.	ÚBICACIÓN: N	PERITAJE: FIRMA	LAMINA: ARQ. 01 ESCALA: 1:100	SUPERFICIES AREA DE TERRENO PLANTA BAJA PLANTA ALTA TOTAL	500m2 306.43m2 24.18m2 330.61m2

ESCALA GRÁFICA.

0 0.10 0.30 0.50 0.75 1 2